


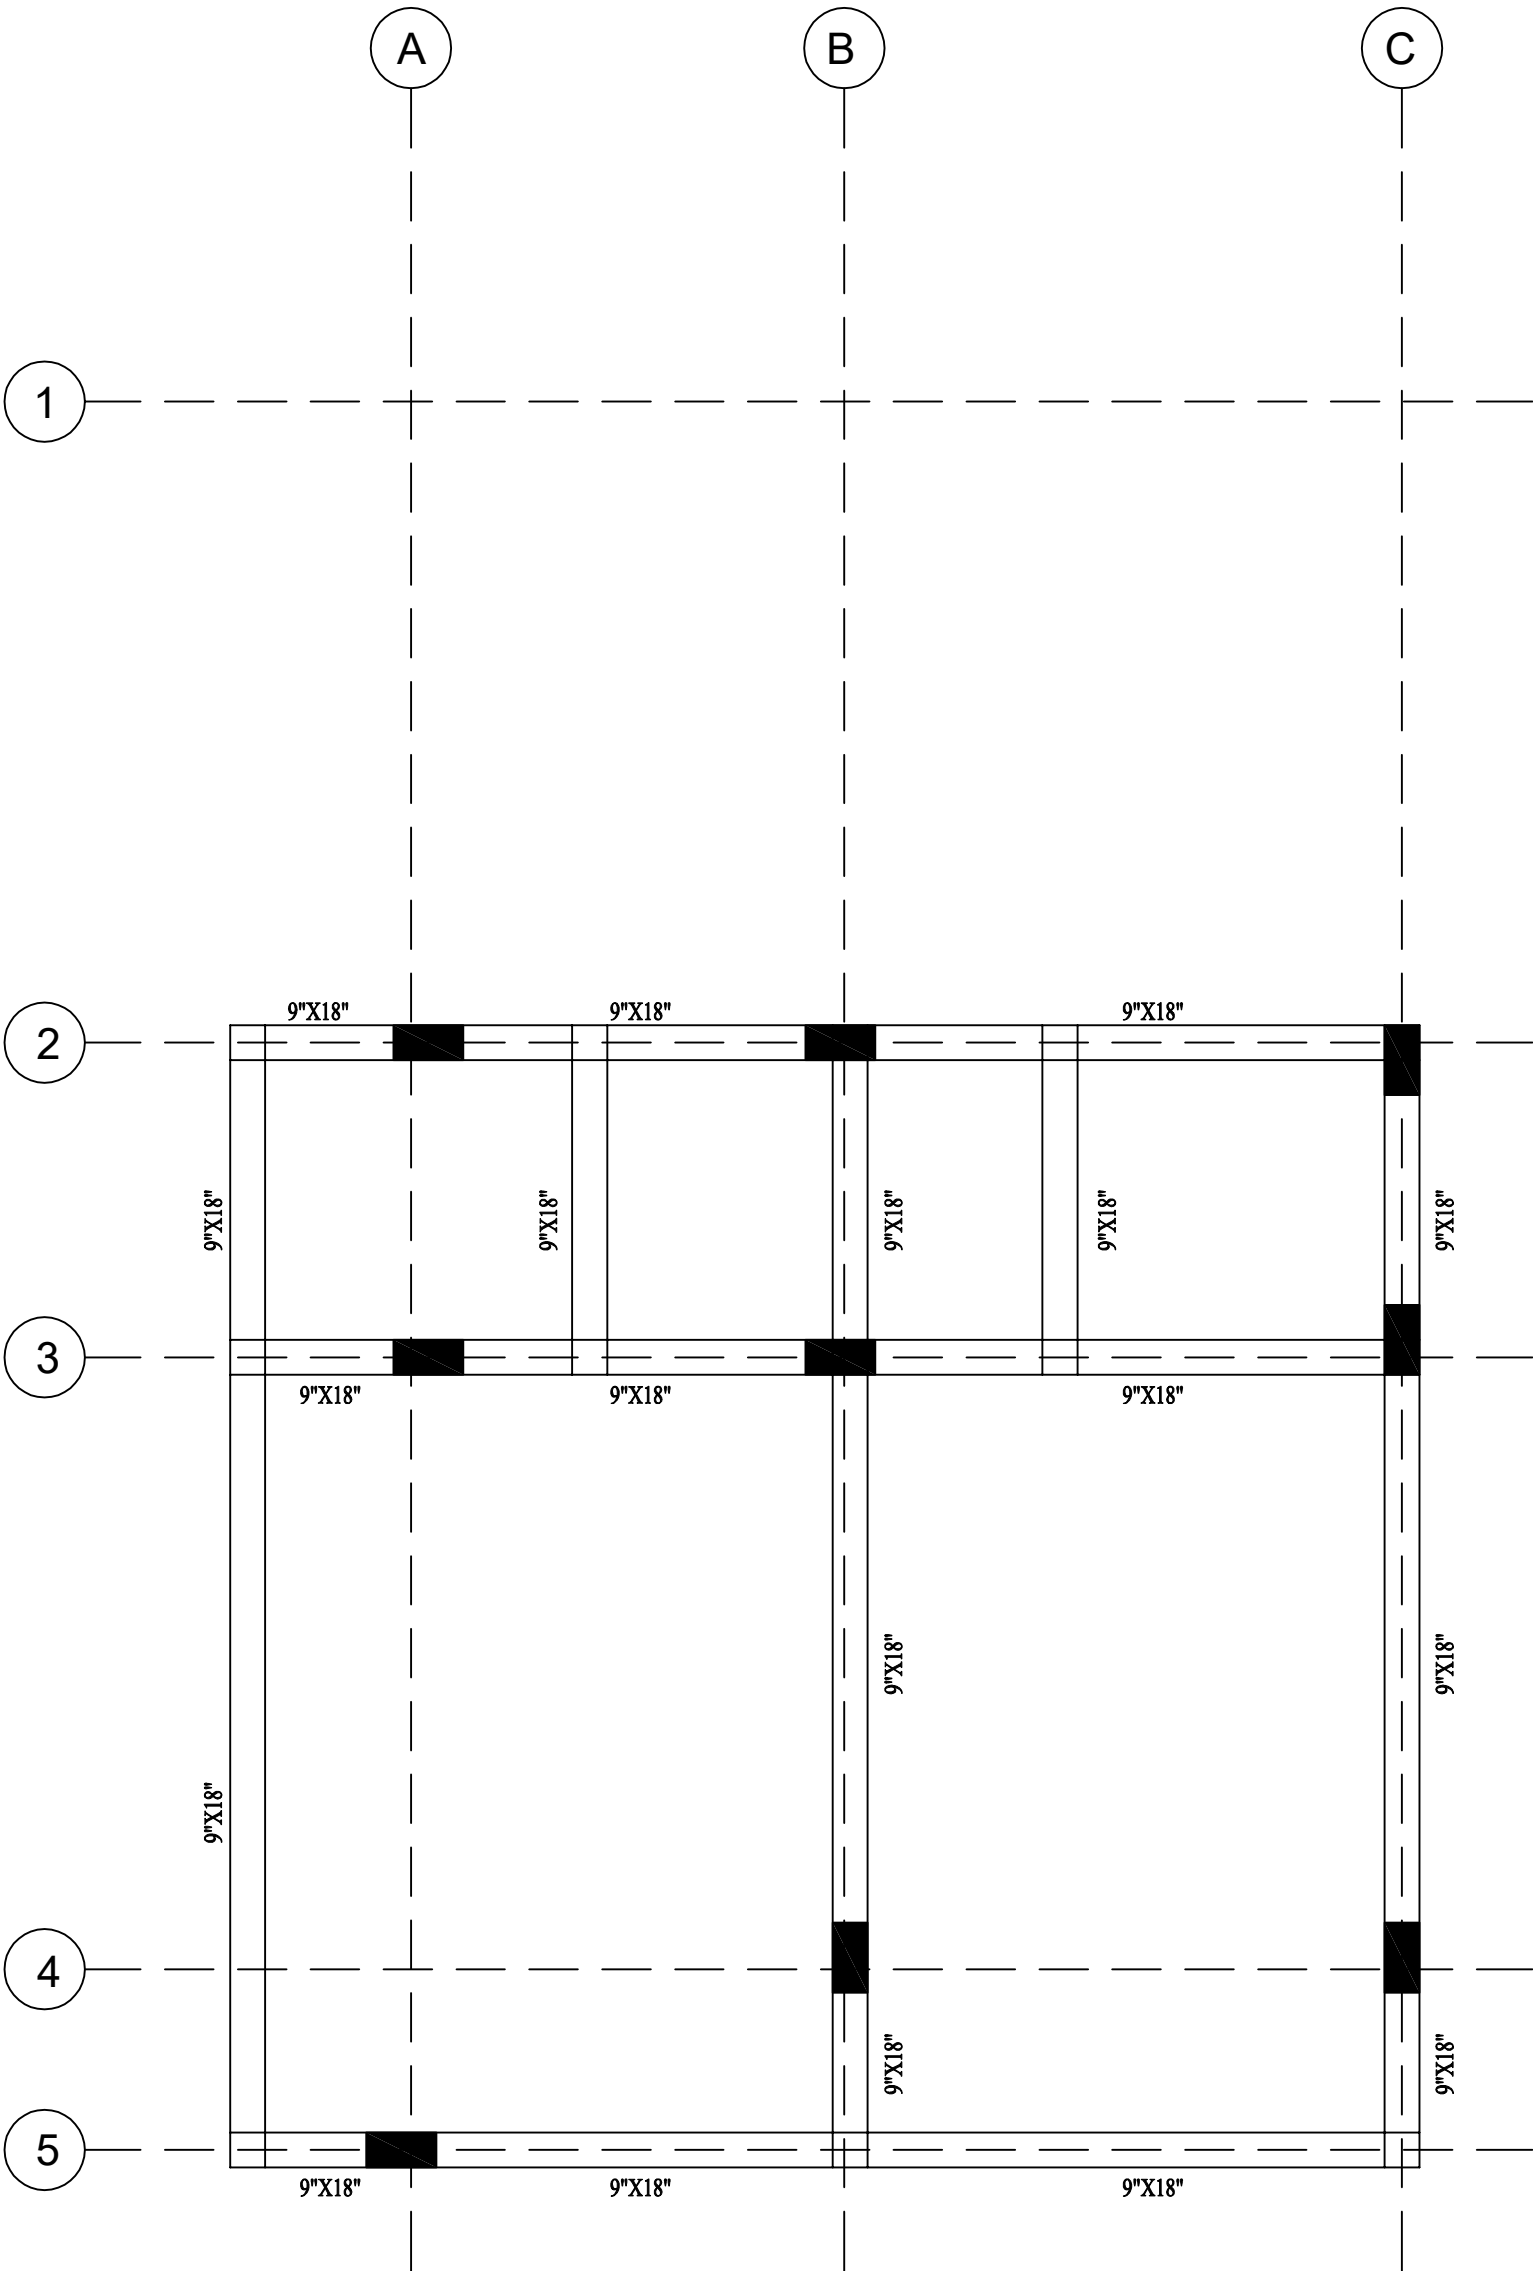

- NOTE:—
1. ALL CONC. SHALL HAVE A COMPRESSIVE STRENGTH OF (M-25) AT 28 DAYS UNLESS NOTED OTHERWISE.
 2. CONC. SHALL BE VIBRATED.
 3. ALL REINF. STEEL USE RIBBED TOR STEEL (T M T) YIELD STRESS 500N/mm2
 4. CONC. CLEAR COVER FOR REINF.
COLUMNS – 40 mm
FOOTINGS – 50 mm
SLABS – 15 mm
BEAMS – 25 mm
 5. IF ANY LOOSE OR FILLED UP SOIL IS FOUND AT SITE ARCHITECT/CLIENT SHOULD BE CONSULTED FOR FURTHER INSTRUCTION FOR CHANGE IN DEPTH OF FOUNDATION.
 6. ALL LAPS TO BE 50XDIA OF BARS.
 7. WATER TO BE TESTED BEFORE STARTING OF WORK
 8. BEARING CAPACITY OF SOIL TO BE ASSUMED 11t/sqm.
 9. STRUCTURE IS DESIGNED FOR GROUND + 3 FLOORS

PROJECT:—

M/S RASHMI PANT

STRUCTURAL CONSULTANT:—

JAY AEDI DEV

H. NO. 80A, WARD NO 8, JAGDAMANAGAR
NEAR DC, HALDWANI-263139

M| 7055676167,6397496096

E| er.darshankumarbhatt@gmail.com

SHEET TITLE GROUND FLOOR ROOF FRAMING PLAN	DATE 09-01-2024
ARCHITECT JAY AEDI DEV H. NO. 80A, WARD NO 8, JAGDAMANAGAR NEAR DC, HALDWANI-263139 M 7055676167,6397496096 E er.darshankumarbhatt@gmail.com	CODE NO.
	DRW. NO. S-03